


LEGEND

- Proposed dwelling: enclosed footprint (main body + garage bay)
- Covered front porch (roof extent; open sides)
- Rear deck (uncovered) and deck stair
- Bulkhead ("size may vary" per AFAB)
- Existing dwelling #199 to be removed
- Setback envelope per ECP (20' front/15' sides/23.2' rear)
- Proposed driveway / apron (conceptual)
- Distance from proposed structure to lot line (ft)
- Existing tree within 3' of footprint or drive

CONCEPT SITE PLAN OVERLAY - NOT FOR CONSTRUCTION - NOT A SURVEY

OPTION 1 - PLAN MIRRORED (GARAGE ON WEST, DRIVEWAY SIDE); HOUSE PARALLEL WITH SIDE LOT LINES

40'x45' main body rotated 6.3 deg clockwise from the sheet vertical (mean bearing of the side lot lines), centred between the 15' side setback lines with its rear wall on the rear setback line. Recommended orientation and side - see notes.
Base drawing: PLACES Associates, Inc. Existing Conditions Plan, Project 5827 / Plan 5827-ECP dated Sept. 11, 2026 (1"=10'). House: AFAB Enterprises 'New Single Family Residence' plan set (file "Carter", sheets 1, 3, 4, 5; 1/4"=1'-0"). Overlay prepared 22 Sept. 2026.

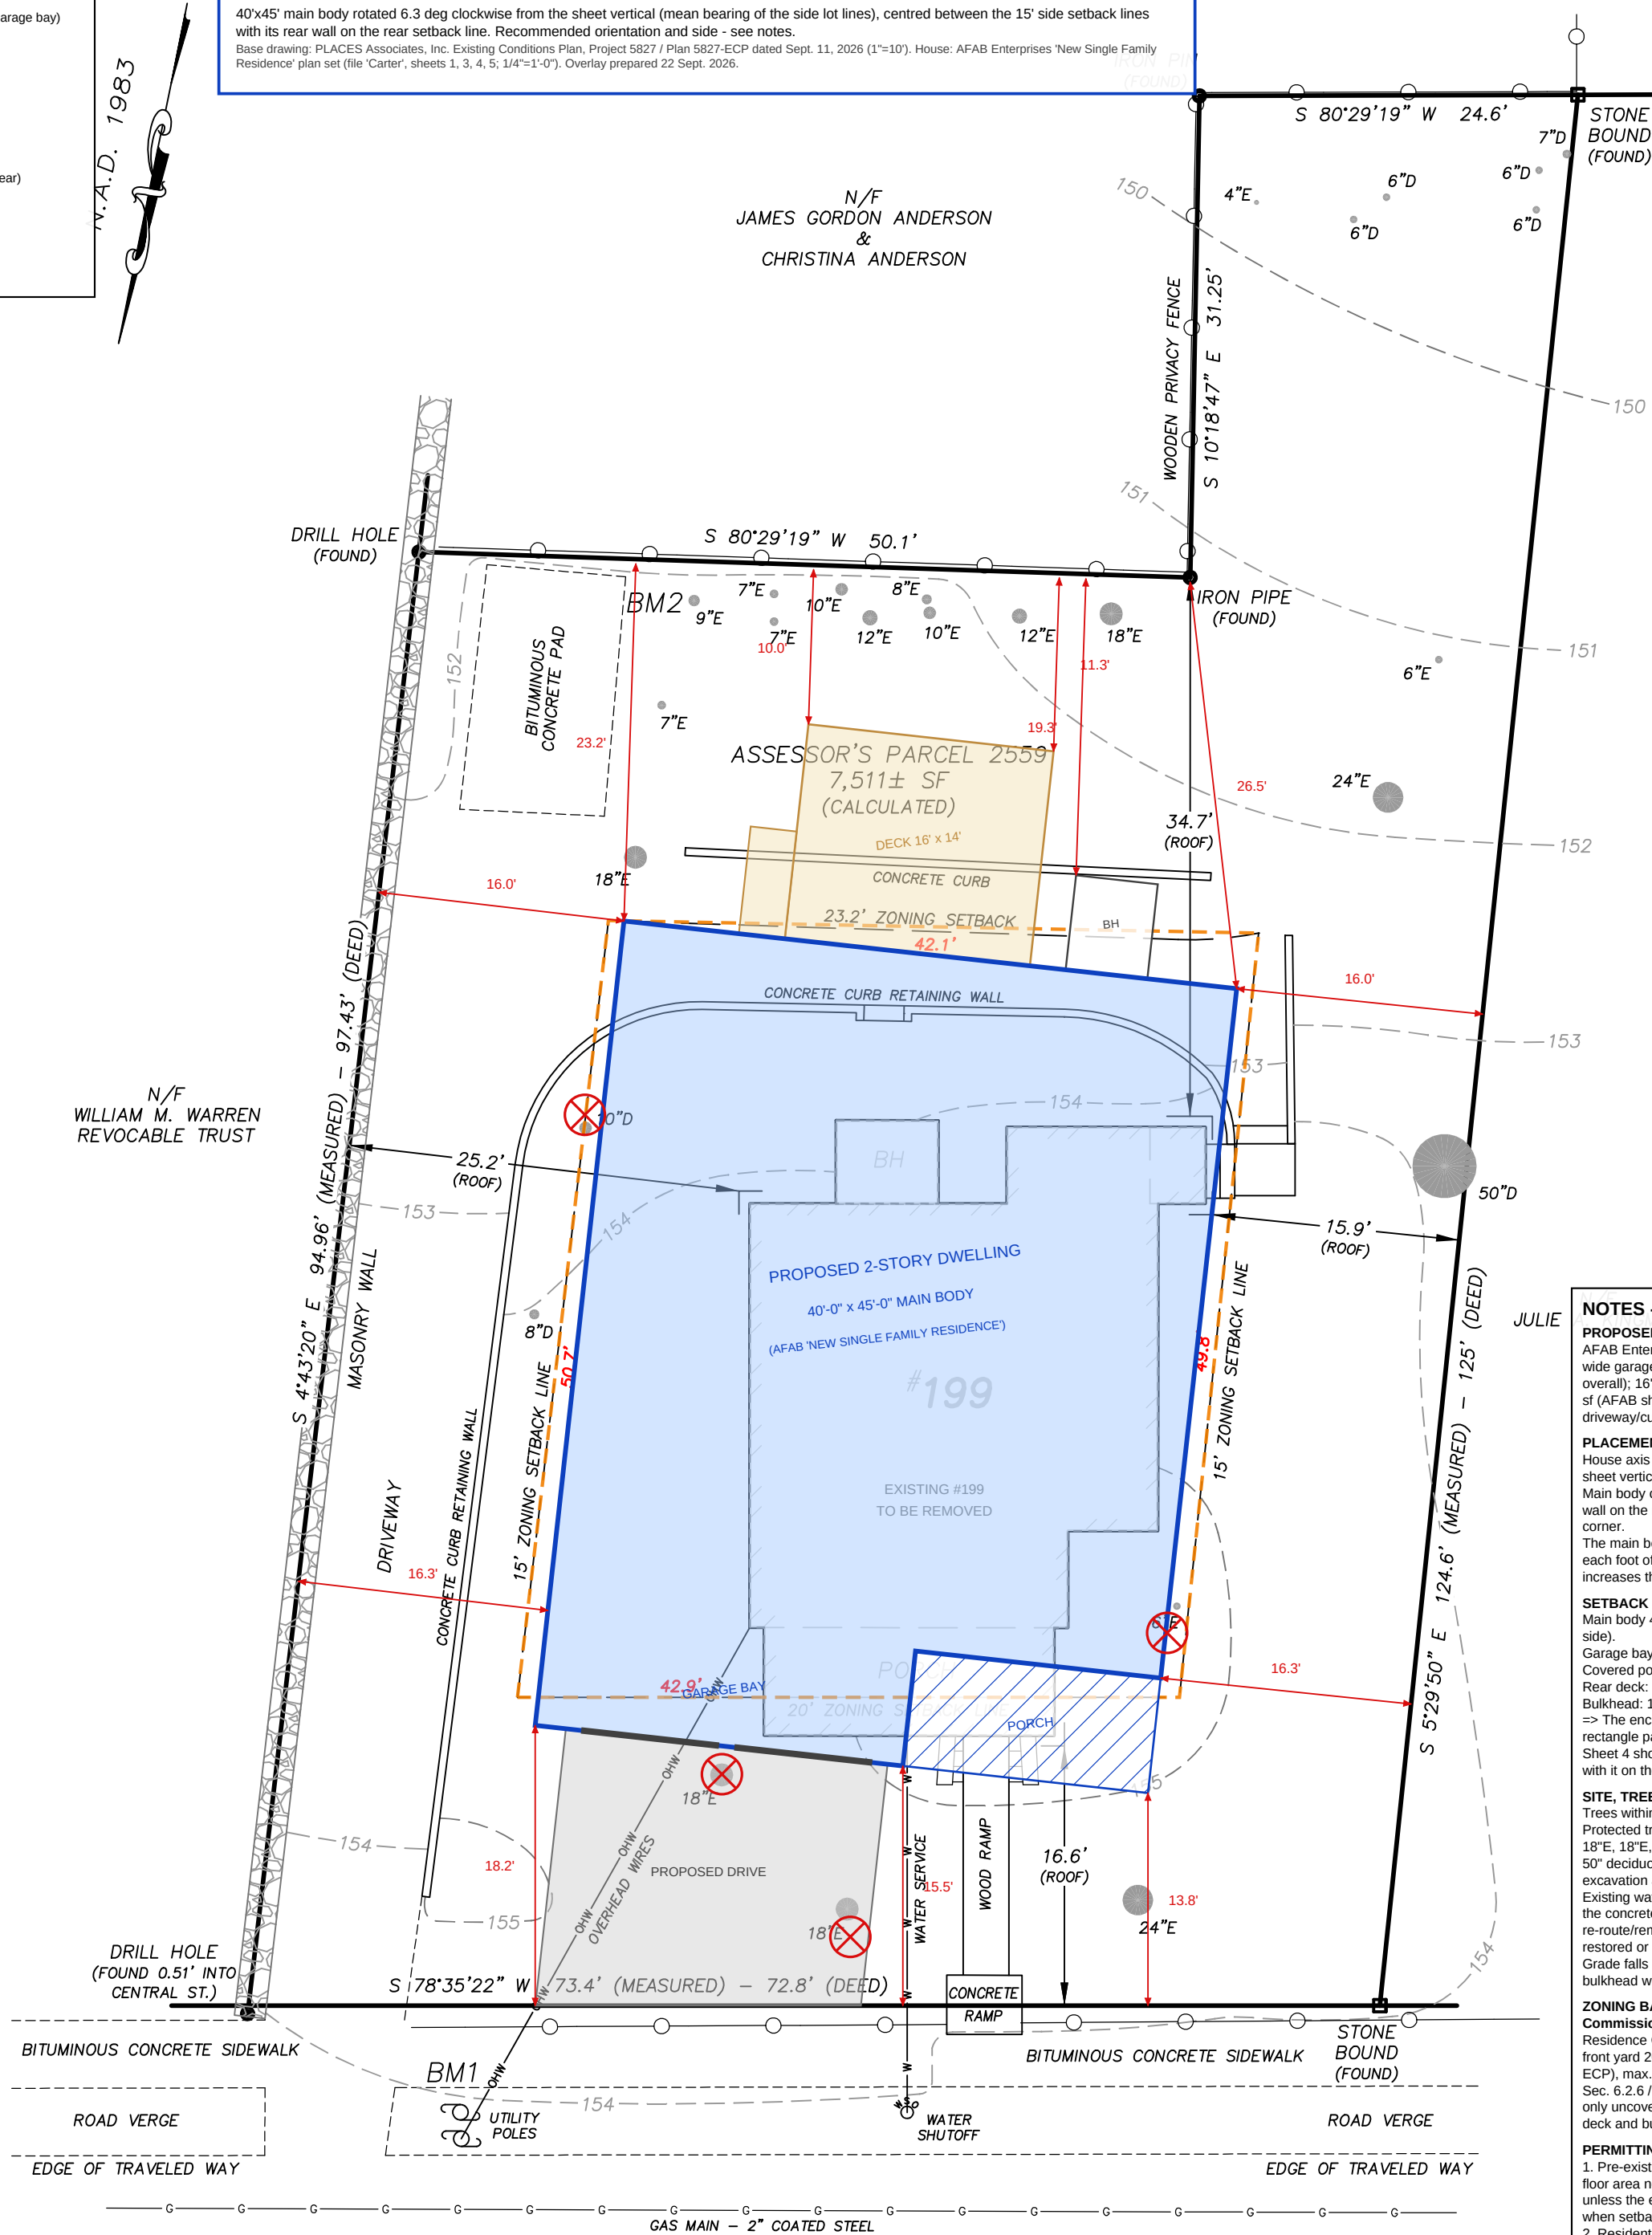

NOTES - OPTION 1

PROPOSED DWELLING

AFAB Enterprises 'New Single Family Residence': 2-story, 40'-0" x 45'-0" main body; 24'-0" wide garage bay and 16'-0" wide covered porch both project 7'-6" toward the street (52'-6" overall); 16' x 14' rear deck; 5'-4" x 6'-2" bulkhead. 1st fl 1,400 sf + 2nd fl 1,987 sf = 3,387 sf (AFAB sheet 4). Plan MIRRORED so the garage is on the WEST (existing driveway/curb-cut side).

PLACEMENT

House axis parallel with the mean bearing of the side lot lines: 6.3 deg clockwise from the sheet vertical (west line S 44-43-20 E leans 6.7 deg, east line S 5-29-50 E leans 5.9 deg). Main body centred between the side setback lines (16.0' / 16.0' to the lot lines) with its rear wall on the rear setback line; main-body front wall 21.2' from Central Street at the east corner. The main body can slide only 1.3' toward the street before it reaches the 20' front line; each foot of slide reduces the rear-yard encroachment of the deck/bulkhead by a foot and increases the front-yard encroachment of the garage/porch by a foot.

SETBACK CHECK (front 20' / sides 15' / rear 23.2')

Main body 40'x45': 21.2' street, 16.0' W, 16.0' E, 23.2' rear - COMPLIES (1.0' spare each side).
Garage bay (WEST): 15.5' to 18.2' from street - 4.5' INSIDE the front setback.
Covered porch (EAST): 13.8' to 15.5' from street - 6.2' INSIDE the front setback.
Rear deck: 10.0' to 11.3' from rear lot line - 13.2' INSIDE the rear setback.
Bulkhead: 19.3' from rear lot line - 3.9' INSIDE the rear setback.
=> The enclosed house as drawn does NOT fit the envelope in any orientation: a 40'-wide rectangle parallel with the lot can be at most ~46.3' deep here, vs. 52'-6" for this plan. Sheet 4 shows the largest front projection that fits (3'-0" with the garage on the west, 1'-3" with it on the east); the memo lists the relief/redesign options.

SITE, TREES, UTILITIES

Trees within 3' of the footprint or drive (marked X): 18"E, 18"E, 6"E, 10"D.
Protected trees (>= 6" DBH in the setback strips, Tree Preservation Bylaw): 50"D, 24"E, 18"E, 18"E, 18"E, 24"E, 10"D, 8"D, 18"E, 12"E.
50" deciduous tree on the east line is ~15' from the nearest proposed structure; keep excavation and the drive out of its root zone (arborist review).
Existing water service (centre of lot), overhead electric from the poles at the SW corner, the concrete-curb retaining wall and the bituminous pad at the rear are all affected - re-route/remove as required. The existing west-side driveway/curb cut can be closed and restored or kept as a parking pad; the new apron needs a CPW driveway permit.
Grade falls ~5' from Central St (el. 155) to the rear line (el. 150-151), so the deck and bulkhead will stand well above grade; AFAB's 'bulkhead size may vary' note applies.

ZONING BASIS (Concord Zoning Bylaw - verify current text with the Building Commissioner)

Residence C, Table III: min. lot 10,000 sf (lot is 7,511 sf), min. frontage 80' (lot has 73.4'), front yard 20', side yards 15', rear yard = lesser of 30' or 25% of lot depth (= 23.2' on the ECP), max. height 35' (mean of plate and ridge, Sec. 6.2.11).
Sec. 6.2.6 / 6.2.8: front and rear yards are measured to the nearest point of ANY structure; only uncovered steps and ramps, walls and fences may cross the line. The covered porch, deck and bulkhead therefore all count against the setbacks.

PERMITTING FLAGS (from bylaw research - confirm with Town staff)

- Pre-existing nonconforming lot: a replacement house over 150% of the existing gross floor area needs a ZBA special permit (Sec. 7.1.5 / 11.6); the 3,387 sf plan is well over that unless the existing house is > 2,258 sf. Precedents show the ZBA routinely grants these when setbacks are met - encroachments (above) weaken the case.
- Residential floor-area cap (Table III / Sec. 6.2.13: sq ft per acre): obtain the Residence C figure - on a 0.17-acre lot it may limit house size before setbacks do.
- Demolition Review: #199 is c.1908 and appears on the West Concord historic resources survey list - Historical Commission review, possible 12-month delay.
- Tree Preservation Bylaw: trees >= 6" DBH with trunks in the setback strips are protected; removal needs a Tree Permit with replanting or \$375/inch mitigation.
- CPW driveway permit for any new/altered curb cut, Engineering sign-off on drainage.

Red dimensions are scaled from the ECP linework (+/- 0.3'); verify by field layout before permitting.

1 INCH = 10 FEET



CHECK SCALE PRIOR TO USING

NOTES:

- ZONING DISTRICT: RESIDENCE "C"
- THE TREES DEPICTED HEREON ARE CLASSIFIED AS EITHER DECIDUOUS "D" OR EVERGREEN "E".
- THE LOCATION OF THE SUBSURFACE UTILITIES ARE SHOWN AS APPROXIMATE AND BASED ON MARKING ON THE GROUND PLACE BY OTHERS.
- THE ELEVATIONS REFER TO THE NORTH AMERICAN VERTICAL DATUM OF 1988 (N.A.V.D. 1988), AND WAS ESTABLISHED WITH THE USE OF GPS EQUIPMENT.

BENCHMARKS: (N.A.V.D. 1988)

BM1 - SPIKE SET 1'± UP IN UTILITY POLE AS SHOWN
ELEVATION = 155.84

BM2 - SPIKE SET 1± UP IN 9" EVERGREEN TREE AS SHOWN
ELEVATION = 153.10

REFERENCES:

- DEED RECORDED IN BOOK 22087, PAGE 181
- PLAN NUMBER 1172 OF 1946
- PLAN NUMBER 960 OF 2013

I HEREBY STATE THAT THE LOCATION OF THE FEATURES SHOWN HEREON IS THE RESULT OF A FIELD SURVEY PERFORMED AS OF SEPTEMBER 3, 2026.

MARC E. CORRIVEAU
PROFESSIONAL
LAND SURVEYOR

DATE:

EXISTING CONDITIONS PLAN

LOCATION: 199 CENTRAL STREET

CITY/TOWN: CONCORD, MASSACHUSETTS

PREPARED FOR:

JEFF SENARIAN

SCALE: 1 INCH = 10 FEET DATE: SEPTEMBER 11, 2026

PLACES Associates, Inc.



• Planning
• Landscape
• Architecture
• Civil
• Engineering
• Surveying
256 Great Road, Suite 4
Littleton, MA 01460
(978) 486-0334
www.placesassociates.com

PROJECT No.: 5827

PLAN No.: 5827 - ECP

LEGEND


- Proposed dwelling: enclosed footprint (main body + garage bay)
- Covered front porch (roof extent; open sides)
- Rear deck (uncovered) and deck stair
- Bulkhead ("size may vary" per AFAB)
- Existing dwelling #199 to be removed
- Setback envelope per ECP (20' front/15' sides/23.2' rear)
- Proposed driveway / apron (conceptual)
- Distance from proposed structure to lot line (ft)
- Existing tree within 3' of footprint or drive

CONCEPT SITE PLAN OVERLAY - NOT FOR CONSTRUCTION - NOT A SURVEY

OPTION 2 - PLAN AS DRAWN (GARAGE ON EAST); HOUSE PARALLEL WITH SIDE LOT LINES

Same placement of the 40'x45' main body as Option 1, plan not mirrored. Shown for comparison of driveway location, trees and the front-yard encroachment of the garage bay.

Base drawing: PLACES Associates, Inc. Existing Conditions Plan, Project 5827 / Plan 5827-ECP dated Sept. 11, 2026 (1"=10'). House: AFAB Enterprises 'New Single Family Residence' plan set (file 'Carter', sheets 1, 3, 4, 5, 1/4"=1'-0"). Overlay prepared 22 Sept. 2026.

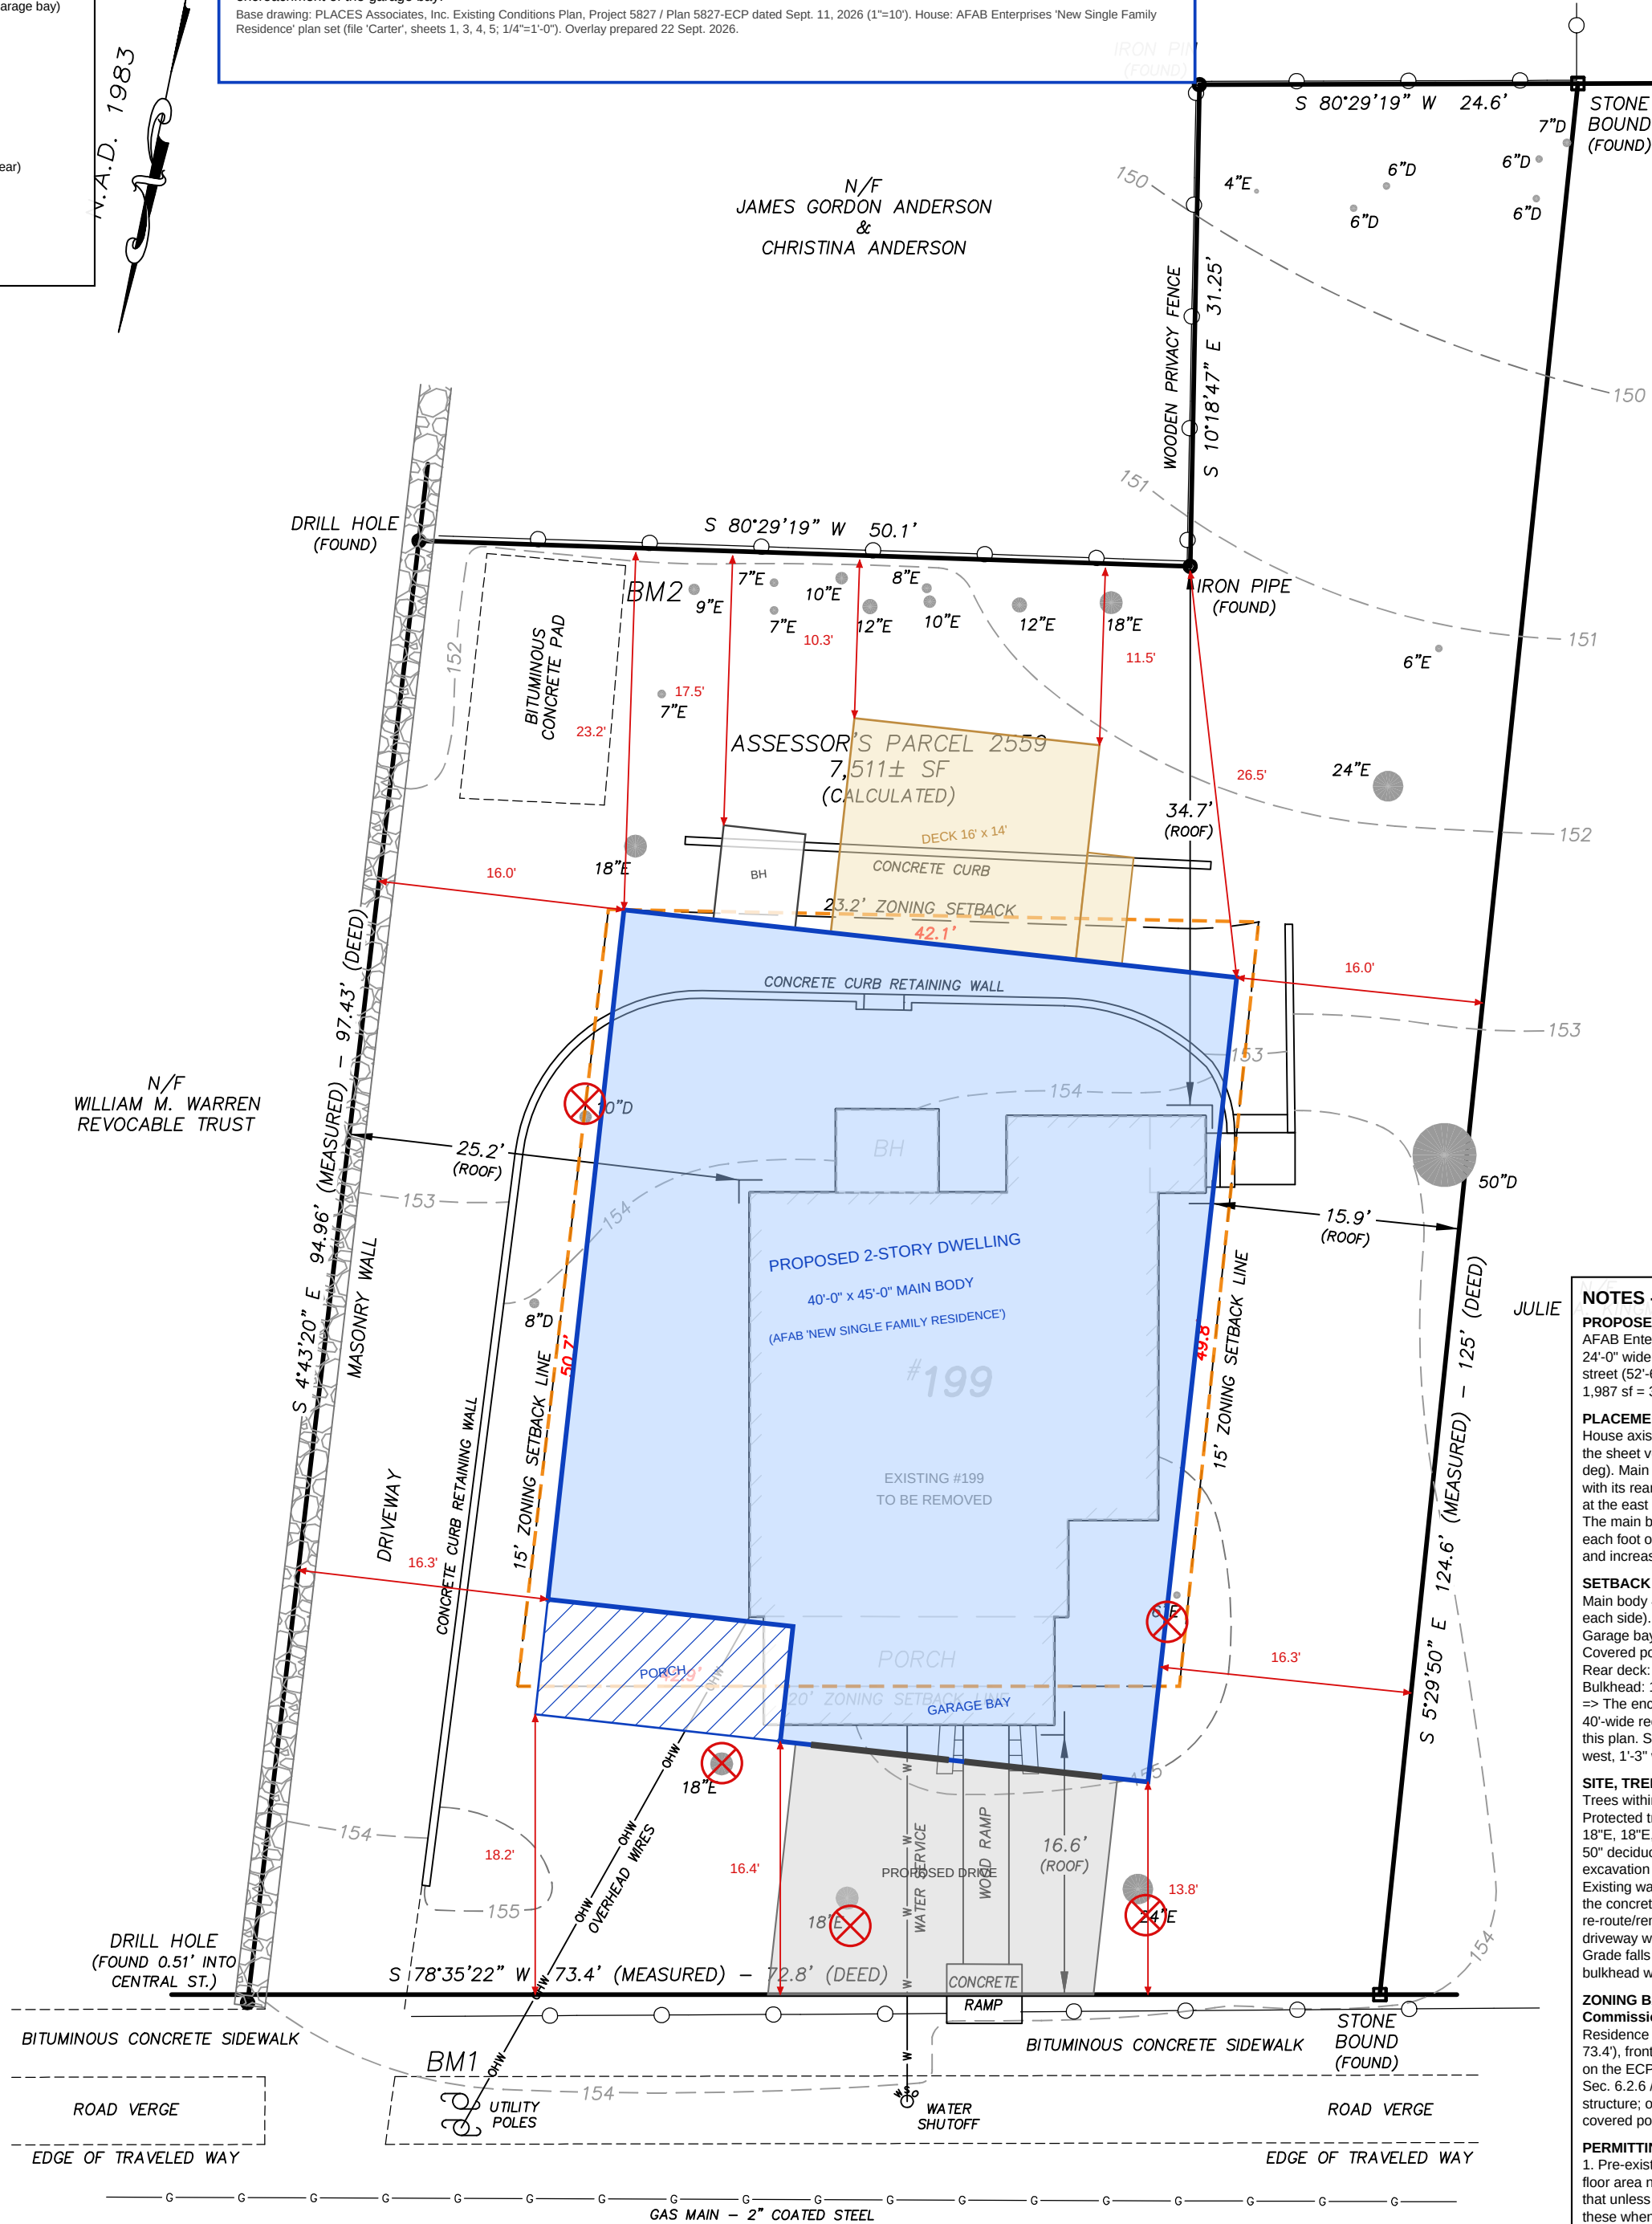

NOTES - OPTION 2

PROPOSED DWELLING

AFAB Enterprises 'New Single Family Residence': 2-story, 40'-0" x 45'-0" main body; 24'-0" wide garage bay and 16'-0" wide covered porch both project 7'-6" toward the street (52'-6" overall); 16' x 14' rear deck; 5'-4" x 6'-2" bulkhead. 1st fl 1,400 sf + 2nd fl 1,987 sf = 3,387 sf (AFAB sheet 4). Plan as drawn, garage on the EAST.

PLACEMENT

House axis parallel with the mean bearing of the side lot lines: 6.3 deg clockwise from the sheet vertical (west line S 4-43-20 E leans 6.7 deg, east line S 5-29-50 E leans 5.9 deg). Main body centred between the side setback lines (16.0' / 16.0' to the lot lines) with its rear wall on the rear setback line; main-body front wall 21.2' from Central Street at the east corner.

The main body can slide only 1.3' toward the street before it reaches the 20' front line; each foot of slide reduces the rear-yard encroachment of the deck/bulkhead by a foot and increases the front-yard encroachment of the garage/porch by a foot.

SETBACK CHECK (front 20' / sides 15' / rear 23.2')

Main body 40'x45': 21.2' street, 16.0' W, 16.0' E, 23.2' rear - COMPLIES (1.0' spare each side).

Garage bay (EAST): 13.8' to 16.4' from street - 6.2' INSIDE the front setback.

Covered porch (WEST): 16.4' to 18.2' from street - 3.6' INSIDE the front setback.

Rear deck: 10.3' to 11.5' from rear lot line - 12.9' INSIDE the rear setback.

Bulkhead: 17.5' from rear lot line - 5.7' INSIDE the rear setback.

=> The enclosed house as drawn does NOT fit the envelope in any orientation: a 40'-wide rectangle parallel with the lot can be at most -46.3' deep here, vs. 52'-6" for this plan. Sheet 4 shows the largest front projection that fits (3'-0" with the garage on the west, 1'-3" with it on the east); the memo lists the relief/redesign options.

SITE, TREES, UTILITIES

Trees within 3' of the footprint or drive (marked X): 24'E, 18'E, 18'E, 6"E, 10"D. Protected trees (>= 6" DBH in the setback strips, Tree Preservation Bylaw): 50"D, 24"E, 18"E, 18'E, 18'E, 24"E, 10"D, 8"D, 18'E, 12"E.

50" deciduous tree on the east line is -15' from the nearest proposed structure; keep excavation and the drive out of its root zone (arborist review).

Existing water service (centre of lot), overhead electric from the poles at the SW corner, the concrete-curb retaining wall and the bituminous pad at the rear are all affected - re-route/remove as required. A new east-side curb cut is needed; the existing west driveway would be abandoned.

Grade falls -5' from Central St (el. 155) to the rear line (el. 150-151), so the deck and bulkhead will stand well above grade; AFAB's 'bulkhead size may vary' note applies.

ZONING BASIS (Concord Zoning Bylaw - verify current text with the Building Commissioner)

Residence C, Table III: min. lot 10,000 sf (lot is 7,511 sf), min. frontage 80' (lot has 73.4', front yard 20', side yards 15', rear yard = lesser of 30' or 25% of lot depth (= 23.2' on the ECP), max. height 35' (mean of plate and ridge, Sec. 6.2.11).

Sec. 6.2.6 / 6.2.8: front and rear yards are measured to the nearest point of ANY structure; only uncovered steps and ramps, walls and fences may cross the line. The covered porch, deck and bulkhead therefore all count against the setbacks.

PERMITTING FLAGS (from bylaw research - confirm with Town staff)

- Pre-existing nonconforming lot: a replacement house over 150% of the existing gross floor area needs a ZBA special permit (Sec. 7.1.5 / 11.6); the 3,387 sf plan is well over that unless the existing house is > 2,258 sf. Precedents show the ZBA routinely grants these when setbacks are met - encroachments (above) weaken the case.
- Residential floor-area cap (Table III / Sec. 6.2.13, sq ft per acre): obtain the Residence C figure - on a 0.17-acre lot it may limit house size before setbacks do.
- Demolition Review: #199 is c.1908 and appears on the West Concord historic resources survey list - Historical Commission review, possible 12-month delay.
- Tree Preservation Bylaw: trees >= 6" DBH with trunks in the setback strips are protected; removal needs a Tree Permit with replanting or \$375/inch mitigation.
- CPW driveway permit for any new/alterd curb cut; Engineering sign-off on drainage.

Red dimensions are scaled from the ECP linework (+/- 0.3'); verify by field layout before permitting.

1 INCH = 10 FEET



CHECK SCALE PRIOR TO USING

NOTES:

- ZONING DISTRICT: RESIDENCE "C"
- THE TREES DEPICTED HEREON ARE CLASSIFIED AS EITHER DECIDUOUS "D" OR EVERGREEN "E".
- THE LOCATION OF THE SUBSURFACE UTILITIES ARE SHOWN AS APPROXIMATE AND BASED ON MARKING ON THE GROUND PLACE BY OTHERS.
- THE ELEVATIONS REFER TO THE NORTH AMERICAN VERTICAL DATUM OF 1988 (N.A.V.D. 1988), AND WAS ESTABLISHED WITH THE USE OF GPS EQUIPMENT.

BENCHMARKS: (N.A.V.D. 1988)

BM1 - SPIKE SET 1'± UP IN UTILITY POLE AS SHOWN
ELEVATION = 155.84

BM2 - SPIKE SET 1'± UP IN 9" EVERGREEN TREE AS SHOWN
ELEVATION = 153.10

REFERENCES:

- DEED RECORDED IN BOOK 22087, PAGE 181
- PLAN NUMBER 1172 OF 1946
- PLAN NUMBER 960 OF 2013

I HEREBY STATE THAT THE LOCATION OF THE FEATURES SHOWN HEREON IS THE RESULT OF A FIELD SURVEY PERFORMED AS OF SEPTEMBER 3, 2026.

MARC E. CORRIVEAU
PROFESSIONAL
LAND SURVEYOR

DATE:

EXISTING CONDITIONS PLAN

LOCATION: 199 CENTRAL STREET

CITY/TOWN: CONCORD, MASSACHUSETTS

PREPARED FOR:

JEFF SENARIAN

SCALE: 1 INCH = 10 FEET DATE: SEPTEMBER 11, 2026

PLACES Associates, Inc.



• Planning
• Landscape
• Architecture
• Civil
• Engineering
• Surveying

256 Great Road, Suite 4
Littleton, MA 01460
(978) 486-0334
www.placesassociates.com

PROJECT No.: 5827


PLAN No.: 5827 - ECP

- LEGEND**
- Main body parallel with side lot lines - fits, ~1.0' spare/side
 - Main body square to Central St - ~1.1' over each side line
 - Setback envelope per ECP
 - Existing dwelling to be removed

CONCEPT SITE PLAN OVERLAY - NOT FOR CONSTRUCTION - NOT A SURVEY

SHEET 3 - ORIENTATION STUDY: PARALLEL WITH THE LOT vs. SQUARE TO CENTRAL STREET

Only the 40' x 45' main body is shown. Blue = rotated 6.3 deg to match the side lot lines (fits). Red dashed = square to the street at its best, balanced position (does not fit). Red = square-to-street distances, blue = parallel distances.
Base drawing: PLACES Associates, Inc. Existing Conditions Plan, Project 5827 / Plan 5827-ECP dated Sept. 11, 2026 (1"=10'). House: AFAB Enterprises 'New Single Family Residence' plan set (file 'Carter', sheets 1, 3, 4, 5, 1/4"=1'-0"). Overlay prepared 22 Sept. 2026.

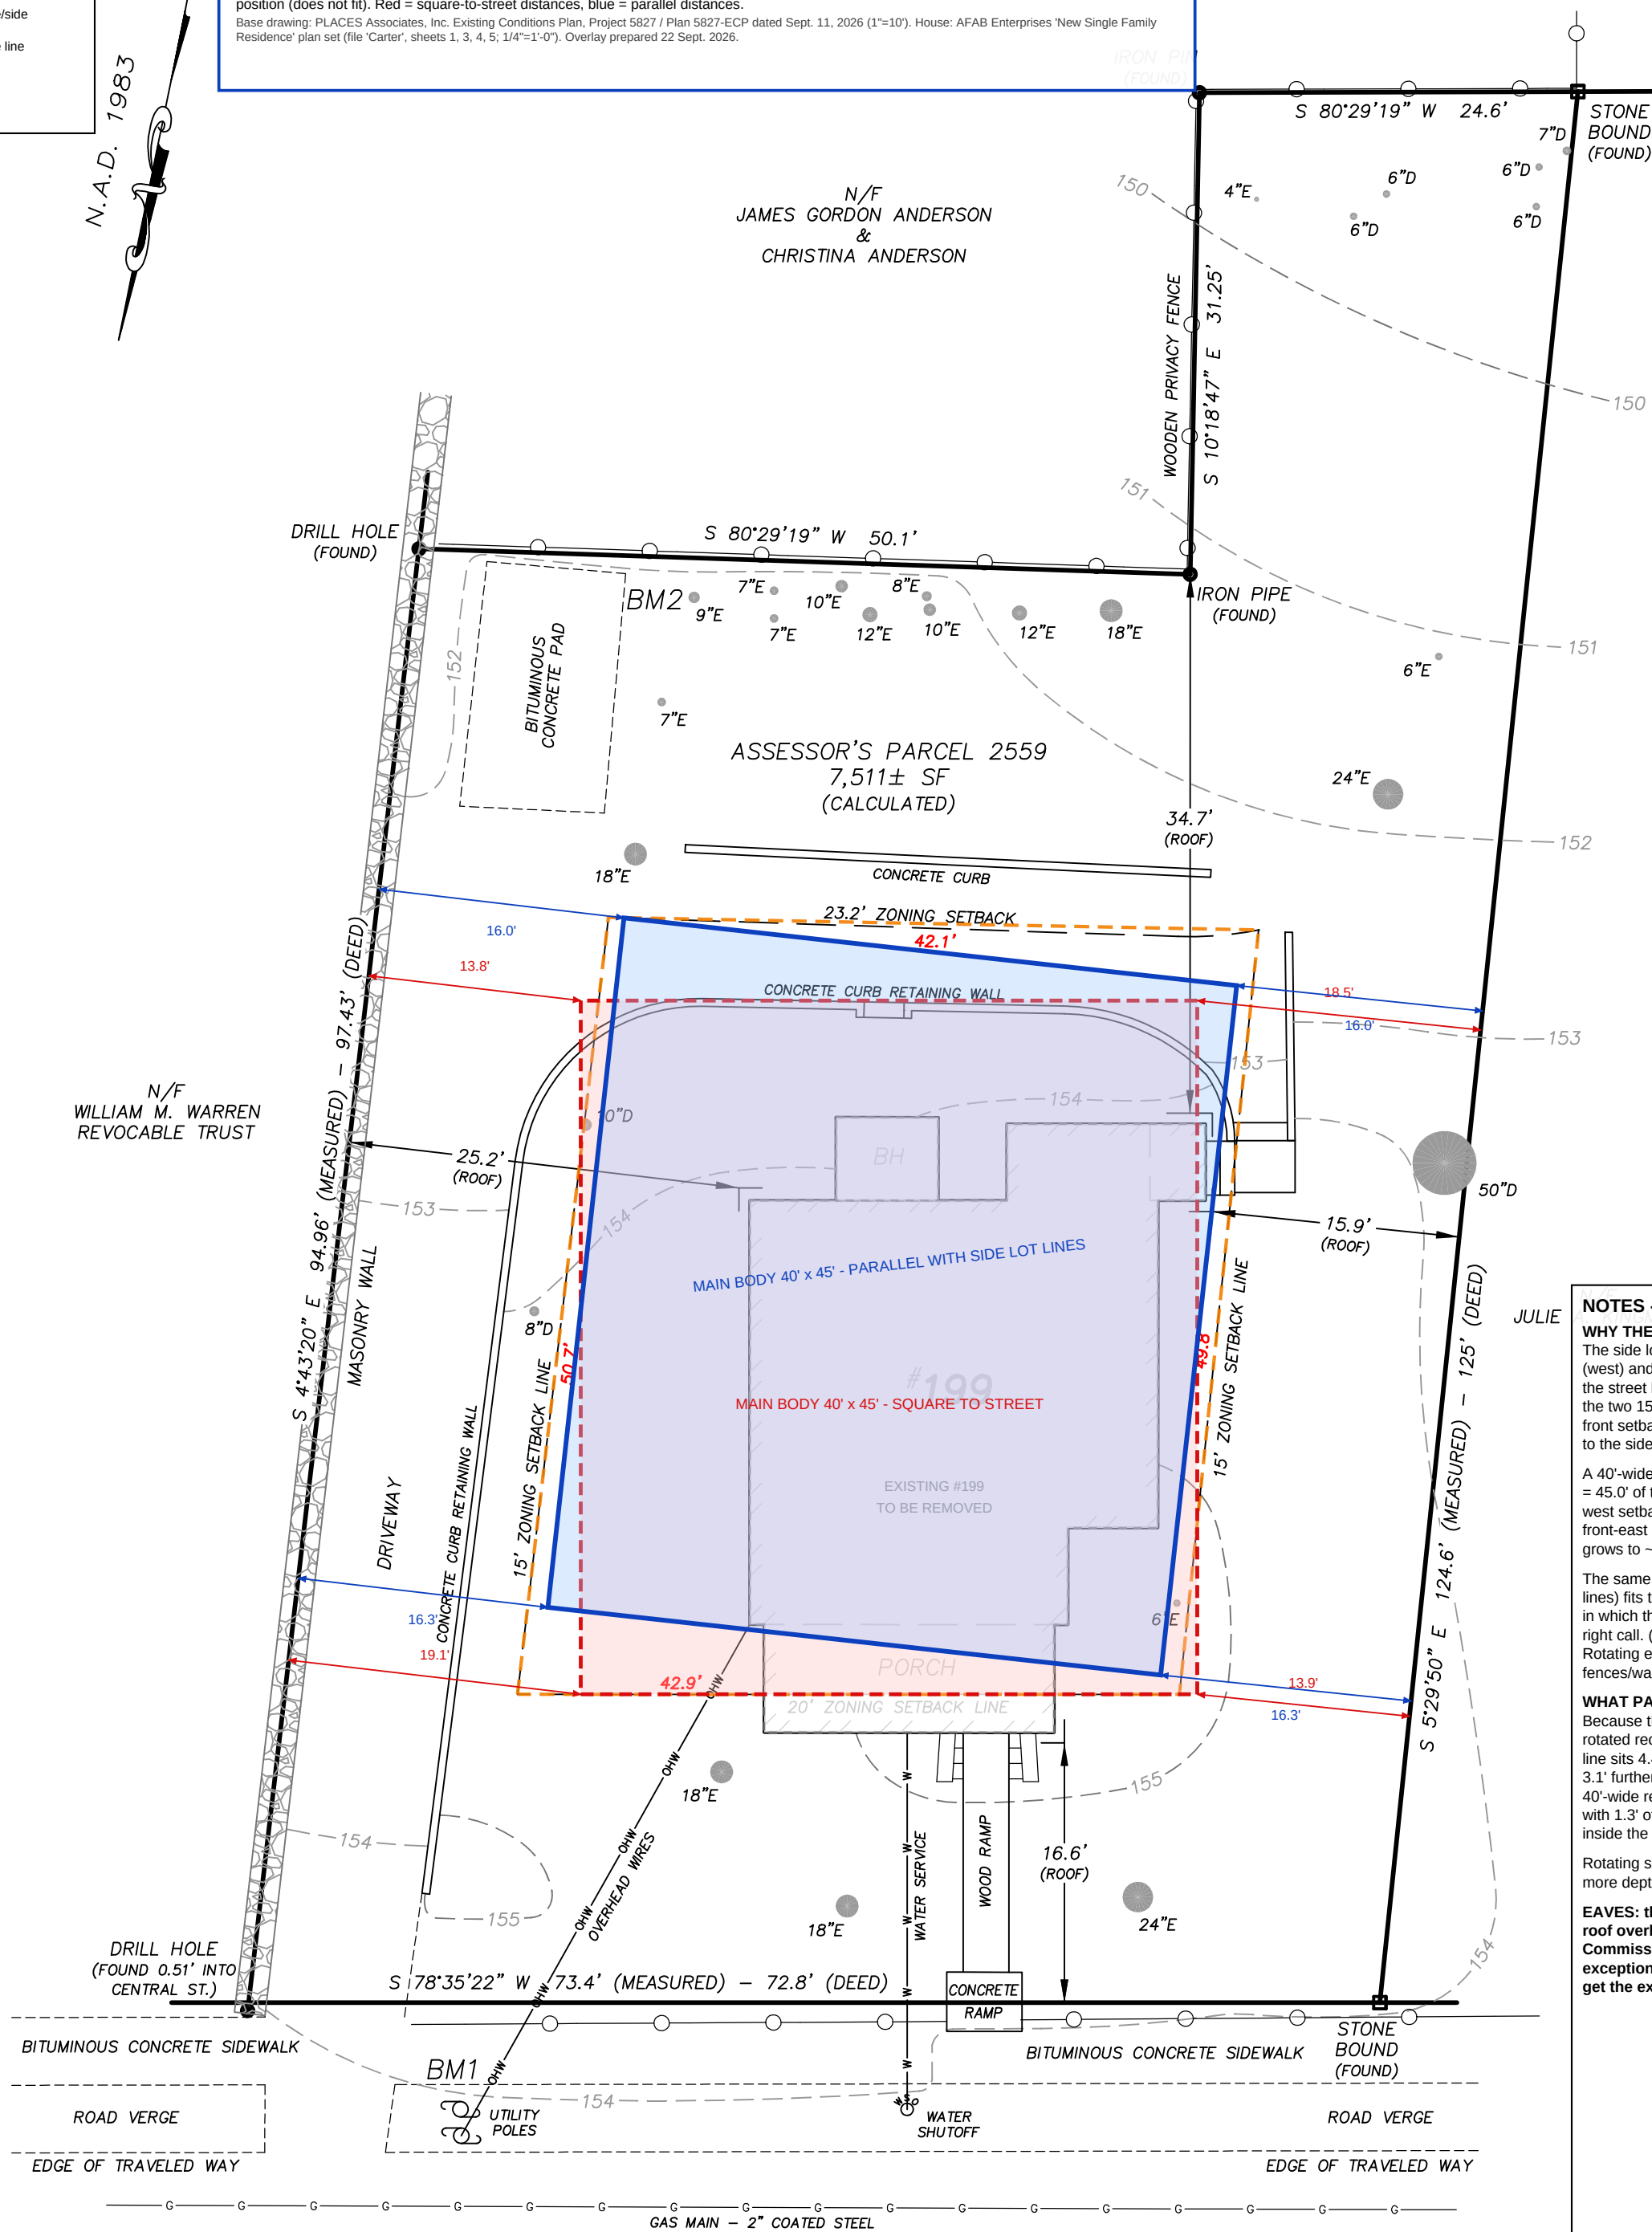

NOTES - ORIENTATION STUDY

WHY THE HOUSE SHOULD BE PARALLEL WITH THE SIDE LOT LINES
The side lot lines are not square to Central Street: on the ECP they lean 6.7 deg (west) and 5.9 deg (east) toward the east as they run away from the street, while the street line runs straight across the sheet. The buildable envelope between the two 15' side setback lines is therefore a slanted strip: 42.9' wide along the front setback line and 42.1' along the rear one, i.e. about 42.4' measured square to the side lines.

A 40'-wide house set SQUARE TO THE STREET needs 40' + 45' x tan(6.3 deg) = 45.0' of that strip over its 45' depth, so it cannot fit: at best it is ~1.1' over the west setback line at its rear-west corner and ~1.1' over the east line at its front-east corner (red). Add the 7'-6" garage/porch projection and the shortfall grows to ~1.5' per side, before any eave overhang.

The same house ROTATED 6.3 deg (parallel with the mean bearing of the side lines) fits the strip with ~1.0' to spare on each side (blue). It is the only orientation in which the 40' width clears both 15' side setbacks, so 'parallel with the lot' is the right call. (The existing house is square to the street, but it is only 27.5' wide.) Rotating exactly parallel also keeps the house visually consistent with the side fences/walls; the ~6 deg skew to the street is barely perceptible from the road.

WHAT PARALLEL COSTS: FRONT-TO-REAR DEPTH

Because the front and rear setback lines are not square to the rotated house, the rotated rectangle loses depth at opposite corners: across the 40' width the front line sits 4.4' further 'back' at the east end than at the west end, and the rear line 3.1' further 'forward' at the west end than at the east. Net effect: a rotated 40'-wide rectangle can be at most ~46.3' deep on this lot. The 45' main body fits with 1.3' of side; the 7'-6" garage/porch projection (52'-6" overall) cannot be held inside the envelope in any orientation.

Rotating slightly less than parallel (about 5.5 deg) trades side clearance for ~0.5' more depth - not enough to matter. Exactly parallel is recommended.

EAVES: the spare side clearance is only ~1.0' per side, so a typical 12"-16" roof overhang lands on or just over the 15' line. Confirm with the Building Commissioner whether eaves count (Sec. 6.2.7 also contains a 3' side-yard exception for low, <= 15'-high portions of the principal structure in Res. C - get the exact text).

1 INCH = 10 FEET



CHECK SCALE PRIOR TO USING

- NOTES:**
- ZONING DISTRICT: RESIDENCE "C"
 - THE TREES DEPICTED HEREON ARE CLASSIFIED AS EITHER DECIDUOUS "D" OR EVERGREEN "E".
 - THE LOCATION OF THE SUBSURFACE UTILITIES ARE SHOWN AS APPROXIMATE AND BASED ON MARKING ON THE GROUND PLACE BY OTHERS.
 - THE ELEVATIONS REFER TO THE NORTH AMERICAN VERTICAL DATUM OF 1988 (N.A.V.D. 1988), AND WAS ESTABLISHED WITH THE USE OF GPS EQUIPMENT.

BENCHMARKS: (N.A.V.D. 1988)
BM1 - SPIKE SET 1'± UP IN UTILITY POLE AS SHOWN
ELEVATION = 155.84
BM2 - SPIKE SET 1'± UP IN 9" EVERGREEN TREE AS SHOWN
ELEVATION = 153.10

- REFERENCES:**
- DEED RECORDED IN BOOK 22087, PAGE 181
 - PLAN NUMBER 1172 OF 1946
 - PLAN NUMBER 960 OF 2013

I HEREBY STATE THAT THE LOCATION OF THE FEATURES SHOWN HEREON IS THE RESULT OF A FIELD SURVEY PERFORMED AS OF SEPTEMBER 3, 2026.

MARC E. CORRIVEAU
PROFESSIONAL
LAND SURVEYOR

DATE:

EXISTING CONDITIONS PLAN

LOCATION: 199 CENTRAL STREET
CITY/TOWN: CONCORD, MASSACHUSETTS
PREPARED FOR:

JEFF SENARIAN

SCALE: 1 INCH = 10 FEET DATE: SEPTEMBER 11, 2026

PLACES Associates, Inc.



• Planning
• Landscape
• Architecture
• Civil
• Engineering
• Surveying
256 Great Road, Suite 4
Littleton, MA 01460
(978) 486-0334
www.placesassociates.com

PROJECT No.: 5827

PLAN No.: 5827 - ECP


LEGEND

- Proposed dwelling: enclosed footprint (main body + garage bay)
- Covered front porch (roof extent, open sides)
- Rear deck (uncovered) and deck stair
- Bulkhead ("size may vary" per AFAB)
- Existing dwelling #199 to be removed
- Setback envelope per ECP (20' front/15' sides/23.2' rear)
- Proposed driveway / apron (conceptual)
- Distance from proposed structure to lot line (ft)
- Existing tree within 3' of footprint or drive
- Original 7'-6" garage/porch projection (reference)

CONCEPT SITE PLAN OVERLAY - NOT FOR CONSTRUCTION - NOT A SURVEY

OPTION 3 - AS OPTION 1 BUT WITH THE FRONT PROJECTIONS CUT BACK (GARAGE 3'-0", PORCH ROOF 1'-3"): THE ENCLOSED HOUSE FITS THE SETBACK ENVELOPE

Garage bay projects 3'-0" and the porch roof 1'-3" instead of 7'-6" (red dashed = original 7'-6" line). Main body, garage and porch roof comply; the rear deck and bulkhead still sit inside the rear setback - see notes.
Base drawing: PLACES Associates, Inc. Existing Conditions Plan, Project 5827 / Plan 5827-ECP dated Sept. 11, 2026 (1"=10'), House: AFAB Enterprises 'New Single Family Residence' plan set (file 'Carter', sheets 1, 3, 4, 5, 1/4"=1'-0"). Overlay prepared 22 Sept. 2026.

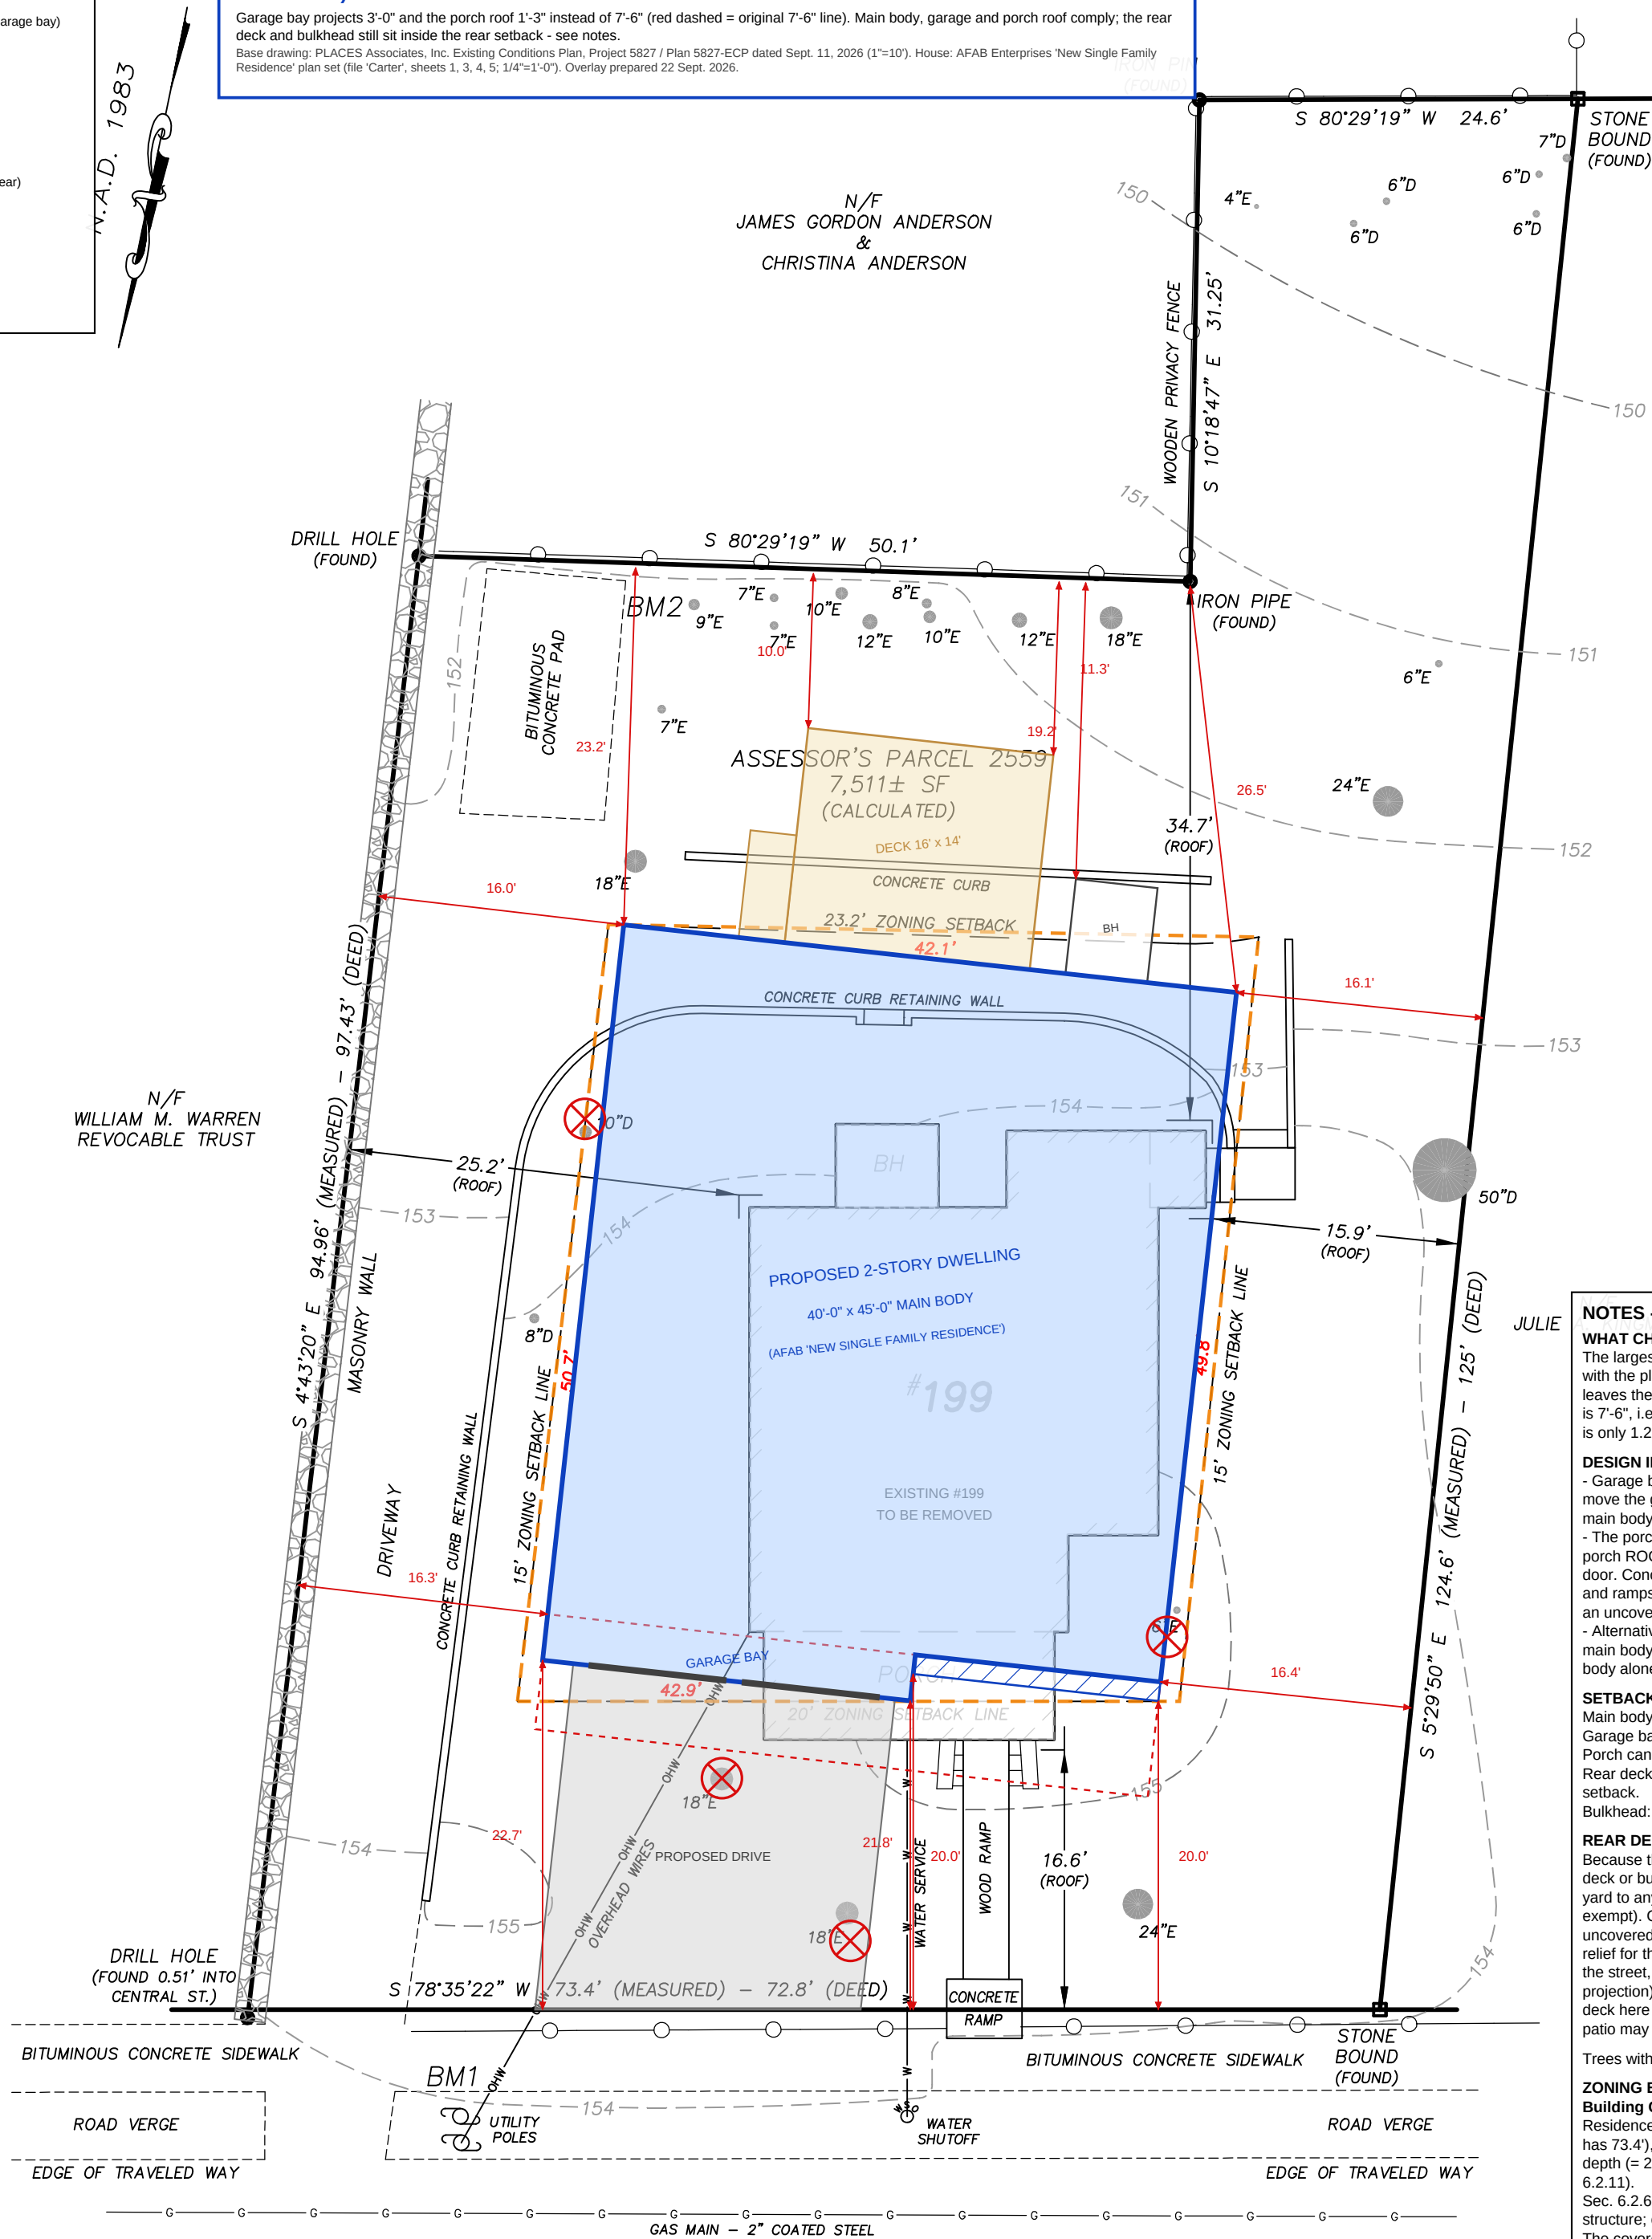

NOTES - OPTION 3

WHAT CHANGED vs. OPTION 1

The largest front projection that keeps the enclosed house inside the envelope, with the plan mirrored (garage on the west, where the skewed front setback line leaves the most room), is 3.05'; it is drawn here as 3'-0". As drawn the projection is 7'-6", i.e. 4.5' too much. With the garage on the EAST (plan as drawn) the limit is only 1.29'.

DESIGN IMPLICATIONS FOR AFAB

- Garage bay clear depth drops from 23'-4" to about 18'-10". To keep a 20'+ bay, move the garage rear wall -1'-2" into the mudroom/bench zone, or shorten the main body by the same amount.

- The porch side (east) has the least front-yard room: with the garage at 3'-0" the porch ROOF can project only 1.29' (drawn as 1'-3"), i.e. an entry canopy over the door. Concord measures the front yard to any structure except uncovered steps and ramps (Sec. 6.2.6), so the 7'-6" covered porch cannot be kept without relief; an uncovered stoop and steps may still project.

- Alternative with the same effect: keep the 7'-6" front projection and shorten the main body from 45' to -40'-6", or drop the projection and lengthen nothing (main body alone has 1.3' of slide).

SETBACK CHECK (front 20' / sides 15' / rear 23.2')

Main body 40'x45': 21.3' street, 16.0' W, 16.1' E, 23.2' rear - COMPLIES.

Garage bay (W): 20.0' to 22.7' from street - COMPLIES.

Porch canopy (E): 20.0' from street at its SE corner - COMPLIES.

Rear deck 16'x14': 10.0' to 11.3' from rear lot line - 13.2' INSIDE the rear setback.

Bulkhead: 19.2' from rear lot line - 4.0' INSIDE the rear setback.

REAR DECK / BULKHEAD

Because the main body's rear wall sits ON the rear setback line, any attached deck or bulkhead is inside the rear setback, and Sec. 6.2.8 measures the rear yard to any structure attached to the dwelling (only uncovered steps/ramps are exempt). Options: (a) replace the deck with an at-grade patio/terrace reached by uncovered steps; (b) shrink the deck to a landing + steps; (c) ask the ZBA for relief for the deck only; (d) drop the bulkhead; grade at the rear is -4'-5" below the street, so a walk-out basement door in the rear foundation wall (no projection) can replace it, or use an interior basement stair. A 14'-deep first-floor deck here would stand -5'-6" above grade at its rail - a walk-out lower level with a patio may suit the site better anyway.

Trees within 3' of the footprint or drive (marked X): 18"E, 18"E, 6"E, 10"D.

ZONING BASIS (Concord Zoning Bylaw - verify current text with the Building Commissioner)
Residence C, Table III: min. lot 10,000 sf (lot is 7,511 sf), min. frontage 80' (lot has 73.4'), front yard 20', side yards 15', rear yard = lesser of 30' or 25% of lot depth (= 23.2' on the ECP), max. height 35' (mean of plate and ridge, Sec. 6.2.11).

Sec. 6.2.6 / 6.2.8: front and rear yards are measured to the nearest point of ANY structure; only uncovered steps and ramps, walls and fences may cross the line. The covered porch, deck and bulkhead therefore all count against the setbacks.

1 INCH = 10 FEET



CHECK SCALE PRIOR TO USING

NOTES:

- ZONING DISTRICT: RESIDENCE "C"
- THE TREES DEPICTED HEREON ARE CLASSIFIED AS EITHER DECIDUOUS "D" OR EVERGREEN "E".
- THE LOCATION OF THE SUBSURFACE UTILITIES ARE SHOWN AS APPROXIMATE AND BASED ON MARKING ON THE GROUND PLACE BY OTHERS.
- THE ELEVATIONS REFER TO THE NORTH AMERICAN VERTICAL DATUM OF 1988 (N.A.V.D. 1988), AND WAS ESTABLISHED WITH THE USE OF GPS EQUIPMENT.

BENCHMARKS: (N.A.V.D. 1988)

BM1 - SPIKE SET 1'± UP IN UTILITY POLE AS SHOWN
ELEVATION = 155.84

BM2 - SPIKE SET 1'± UP IN 9" EVERGREEN TREE AS SHOWN
ELEVATION = 153.10

REFERENCES:

- DEED RECORDED IN BOOK 22087, PAGE 181
- PLAN NUMBER 1172 OF 1946
- PLAN NUMBER 960 OF 2013

I HEREBY STATE THAT THE LOCATION OF THE FEATURES SHOWN HEREON IS THE RESULT OF A FIELD SURVEY PERFORMED AS OF SEPTEMBER 3, 2026.

MARC E. CORRIVEAU
PROFESSIONAL
LAND SURVEYOR

DATE:

EXISTING CONDITIONS PLAN

LOCATION: 199 CENTRAL STREET

CITY/TOWN: CONCORD, MASSACHUSETTS

PREPARED FOR:

JEFF SENARIAN

SCALE: 1 INCH = 10 FEET DATE: SEPTEMBER 11, 2026

PLACES Associates, Inc.



• Planning
• Landscape
• Architecture
• Civil
• Engineering
• Surveying
256 Great Road, Suite 4
Littleton, MA 01460
(978) 486-0334
www.placesassociates.com

PROJECT No.: 5827

PLAN No.: 5827 - ECP